
AIRCRAFT PARKING / DOCKING CHART - ICAO

AERODROME ELEV:	36' 11.1m	CURAÇAO CONTROL	124.1/127.1
MAIN APRON AVG ELEV:	27' 8.2m	CURAÇAO TERMINAL	119.8
GA APRON AVG ELEV:	26' 8.1m	HATO TWR	118.3
		HATO ATIS	132.6

SURFACE STRENGHT (concrete and asphalt):

RWY	760/F/B/X/T	Main apron	540/F/B/X/T	GA apron	54/F/C/Y/T
TWY	870/F/C/X/T	Cargo apron	750/F/A/X/T		

AEROPUERTO HATO (TNCC)
WILLEMSTAD, CURAÇAO

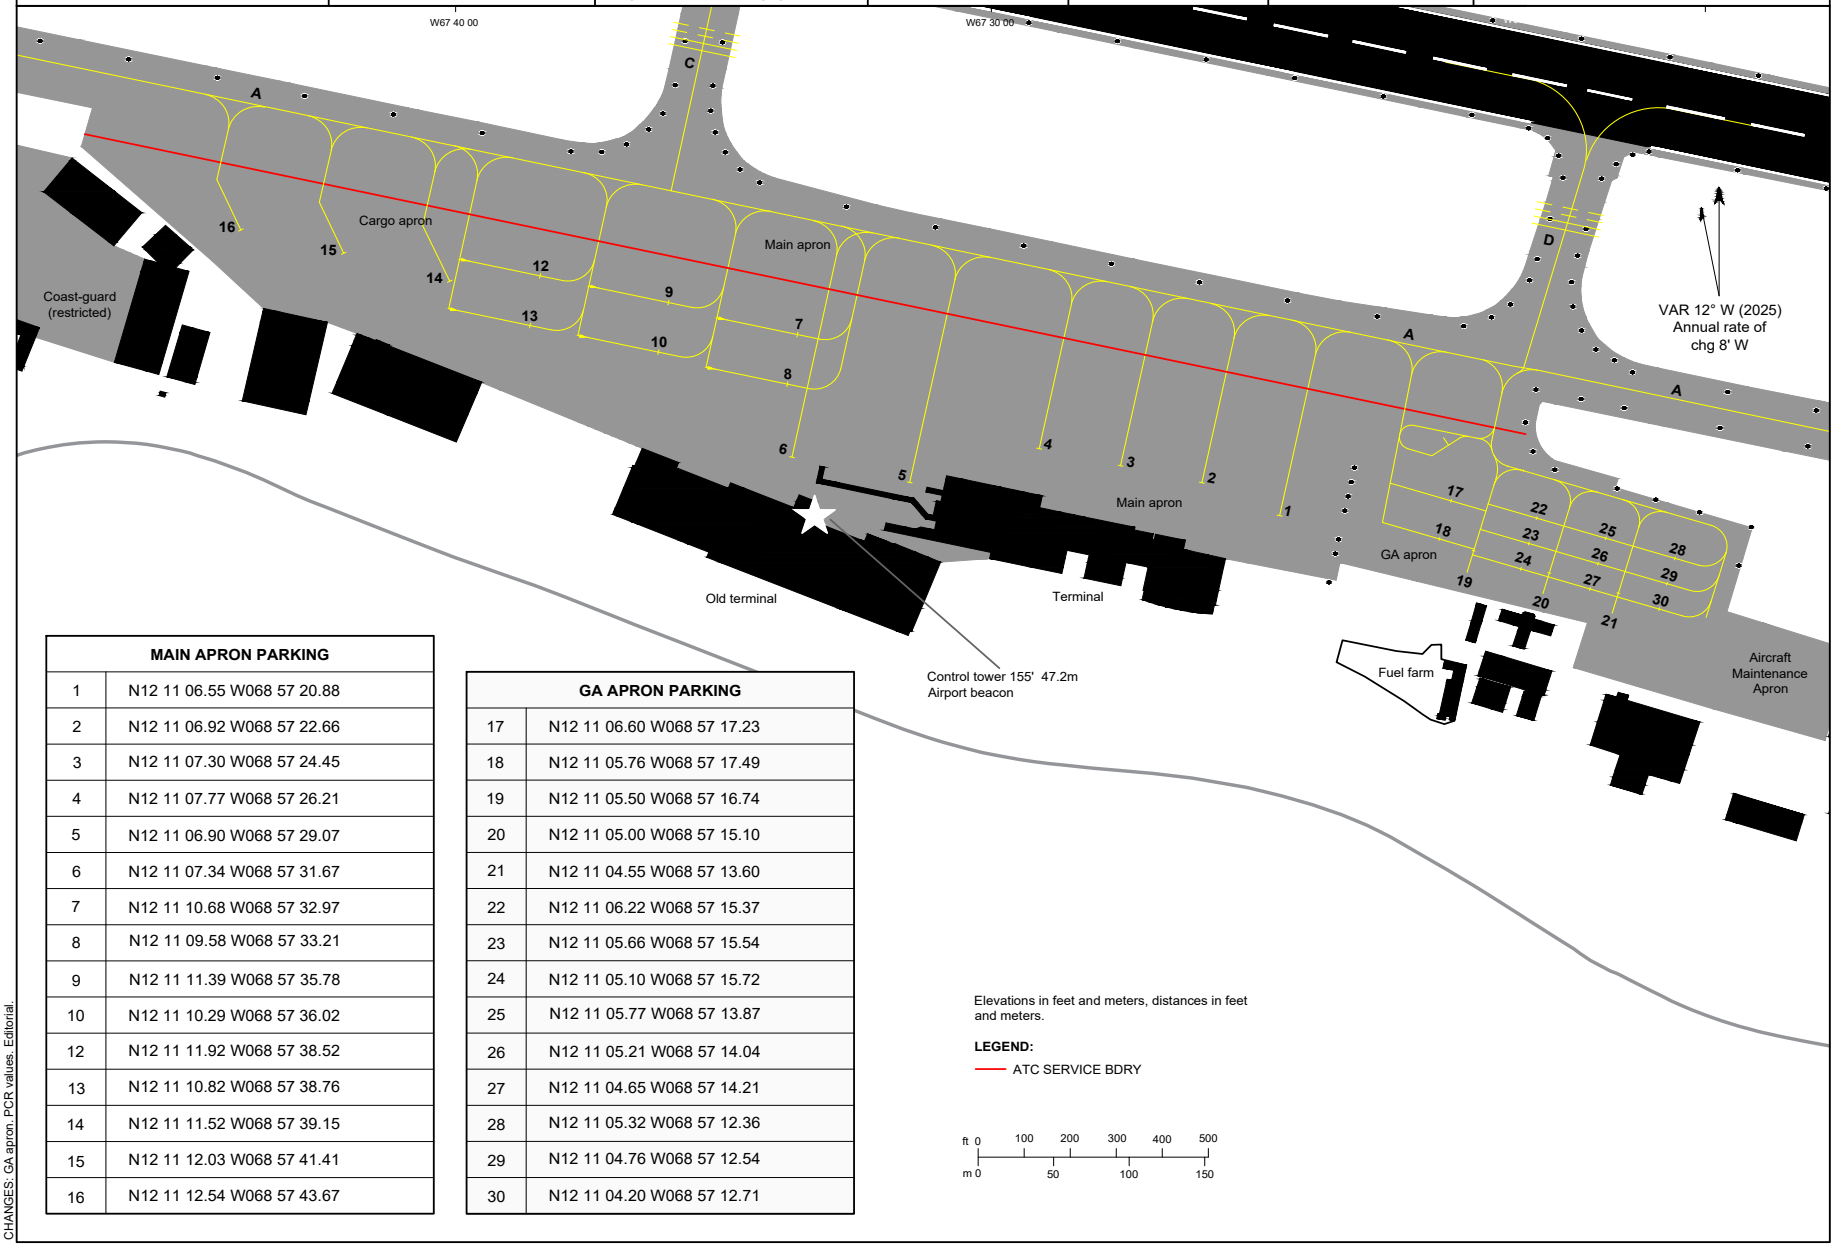

MAIN APRON PARKING	
1	N12 11 06.55 W068 57 20.88
2	N12 11 06.92 W068 57 22.66
3	N12 11 07.30 W068 57 24.45
4	N12 11 07.77 W068 57 26.21
5	N12 11 06.90 W068 57 29.07
6	N12 11 07.34 W068 57 31.67
7	N12 11 10.68 W068 57 32.97
8	N12 11 09.58 W068 57 33.21
9	N12 11 11.39 W068 57 35.78
10	N12 11 10.29 W068 57 36.02
12	N12 11 11.92 W068 57 38.52
13	N12 11 10.82 W068 57 38.76
14	N12 11 11.52 W068 57 39.15
15	N12 11 12.03 W068 57 41.41
16	N12 11 12.54 W068 57 43.67

GA APRON PARKING	
17	N12 11 06.60 W068 57 17.23
18	N12 11 05.76 W068 57 17.49
19	N12 11 05.50 W068 57 16.74
20	N12 11 05.00 W068 57 15.10
21	N12 11 04.55 W068 57 13.60
22	N12 11 06.22 W068 57 15.37
23	N12 11 05.66 W068 57 15.54
24	N12 11 05.10 W068 57 15.72
25	N12 11 05.77 W068 57 13.87
26	N12 11 05.21 W068 57 14.04
27	N12 11 04.65 W068 57 14.21
28	N12 11 05.32 W068 57 12.36
29	N12 11 04.76 W068 57 12.54
30	N12 11 04.20 W068 57 12.71

Elevations in feet and meters, distances in feet and meters.

LEGEND:

ATC SERVICE BDRY

ft 0 100 200 300 400 500
m 0 50 100 150

CHANGES: GA apron. PCR values. Editorial.

AERO INFO DATE 27 NOV 2025