
AIRCRAFT PARKING / DOCKING CHART - ICAO


MAIN APRON AVG ELEV: 65
APRON WITH PKG 16,17: 53
GA APRON AVG ELEV: 31

ATIS 132.1 TOWER 118.0
APRON 121.6 APP 120.9
RFFS 121.7

SURFACE STRENGHT (all asphalt):
Main apron (stand 1-9) 66/R/A/W/T
Main apron (stand 11-17) 64/R/B/W/T
Main apron (stand 23-24) 66/R/A/W/T
GA apron 26/F/A/X/T
Taxiway and runway strength available in AD 2 TNCA-25 (ADC)

REINA BEATRIX INT'L (TNCA)
ORANJESTAD, ARUBA

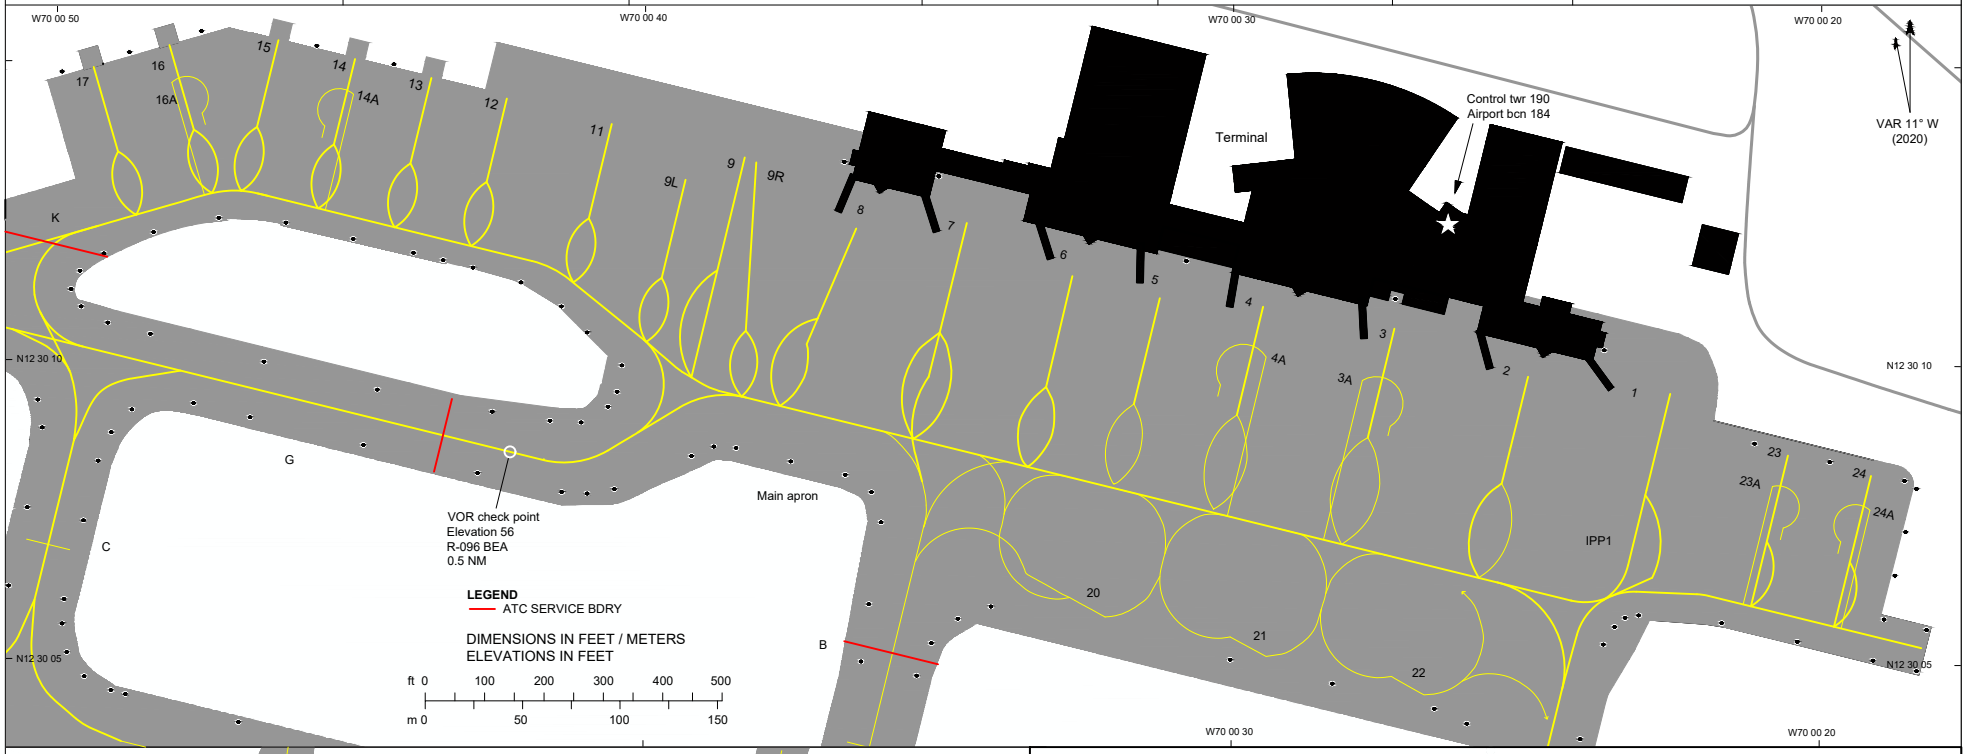

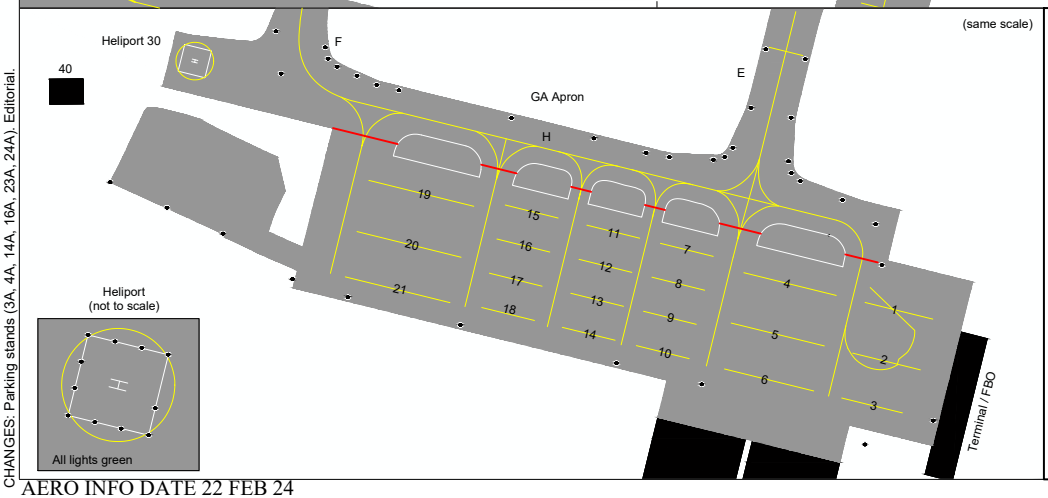

(same scale)

MAIN APRON PARKING	
1	N12 30 09.64 W070 00 22.51
2	N12 30 09.77 W070 00 24.95
3	N12 30 10.58 W070 00 27.25
3A	N12 30 09.71 W070 00 27.78
4	N12 30 10.90 W070 00 29.48
4A	N12 30 10.09 W070 00 29.41
5	N12 30 11.08 W070 00 31.24
6	N12 30 11.44 W070 00 32.73
7	N12 30 12.27 W070 00 34.53
8	N12 30 12.27 W070 00 36.38
9	N12 30 13.38 W070 00 38.28
9L	N12 30 13.01 W070 00 39.29
9R	N12 30 13.31 W070 00 38.08
11	N12 30 13.93 W070 00 40.54
12	N12 30 14.36 W070 00 42.33
13	N12 30 14.68 W070 00 43.64
14	N12 30 15.01 W070 00 44.94
14A	N12 30 14.47 W070 00 44.95
15	N12 30 15.31 W070 00 46.24
16	N12 30 15.24 W070 00 48.10
16A	N12 30 14.66 W070 00 48.04
17	N12 30 14.87 W070 00 49.38
20	N12 30 05.74 W070 00 32.15
21	N12 30 05.09 W070 00 29.41
22	N12 30 04.46 W070 00 26.72
23	N12 30 08.41 W070 00 20.57
23A	N12 30 07.95 W070 00 20.82
24	N12 30 08.08 W070 00 19.17
24A	N12 30 07.55 W070 00 19.16
Heli	N12 29 59.08 W070 00 53.67

CHANGES: Parking stands (3A, 4A, 14A, 16A, 23A, 24A). Editorial.
AERO INFO DATE 22 FEB 24