
AERODROME CHART - ICAO	ARP: N 12 07 50.91 W 068 16 02.71	AERODROME ELEV: 24' 7.4m	CURAÇAO CONTROL 124.1/127.1 CURAÇAO TERMINAL 119.8	FLAMINGO TOWER 118.7 FLAMINGO ATIS 132.3	DIMENSIONS IN FEET/METERS ELEVATIONS IN FEET BEARINGS ARE MAGNETIC	FLAMINGO AIRPORT (TNCB) KRALENDIJK, BONAIRE

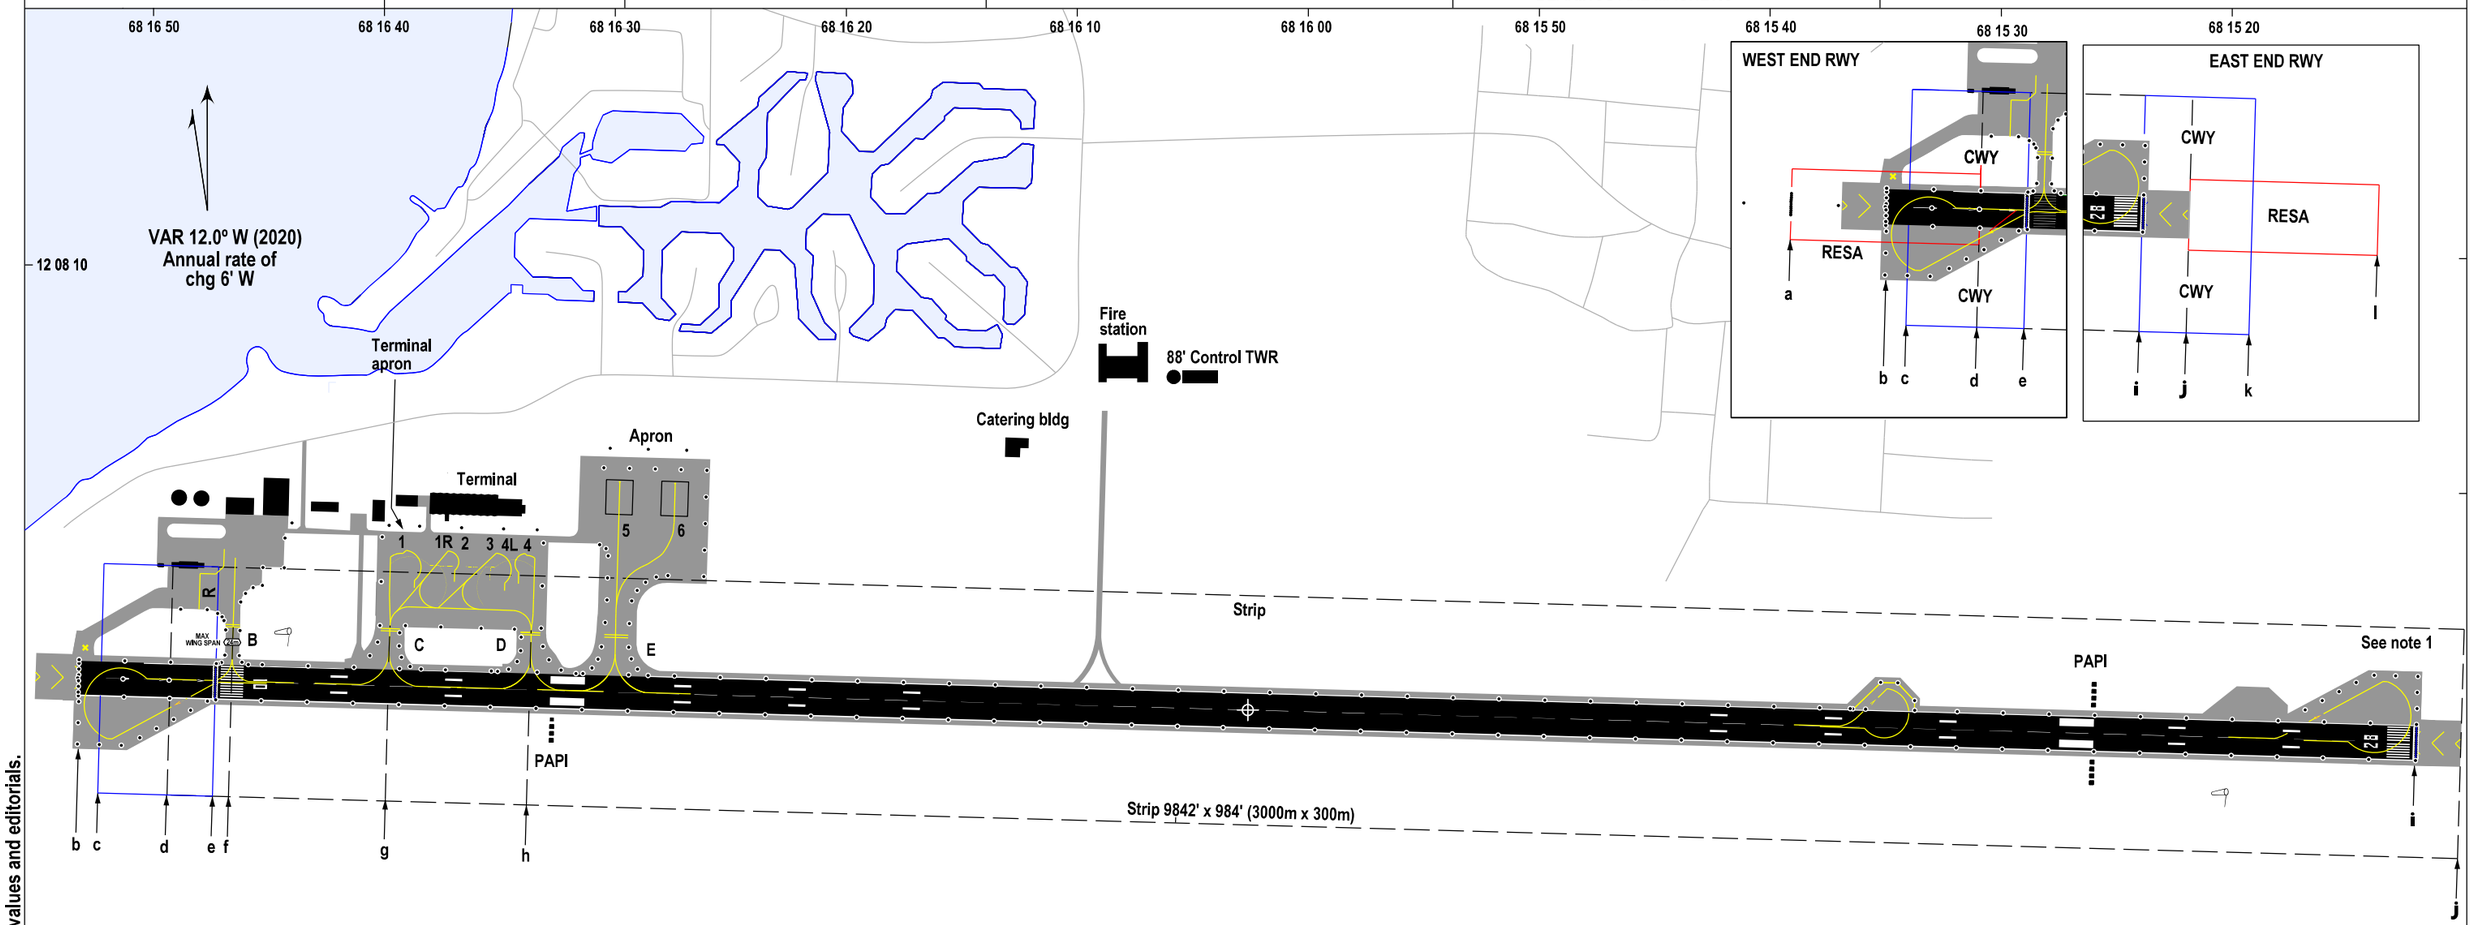

ACFT PARKING COORDINATES	
1	N 12 07 57.75 W 68 16 39.18
1R	N 12 07 57.16 W 68 16 37.90
2	N 12 07 57.74 W 68 16 37.33
3	N 12 07 57.64 W 68 16 35.28
4	N 12 07 57.64 W 68 16 33.92
4L	N 12 07 57.09 W 68 16 35.46
5	N 12 08 00.69 W 68 16 29.86
5D	N 12 08 00.20 W 68 16 29.87
6	N 12 08 00.62 W 68 16 27.46
6D	N 12 08 00.13 W 68 16 27.48

Apron surface and strength		
Designator	Surface	Strength
Main Apron	Concrete and asphalt	PCR 459 F/B/W/U
TNCB B - Aircraft Parking Stands 1-4	Concrete	PCR 600 R/B/W/U
TNCB C- Aircraft Parking Stand 5	Concrete	PCR 921 R/D/W/T
TNCB D - Aircraft Parking Stand 6	Concrete	PCR 921 /R/D/W/T
TNCB E - General Aviation Ramp	Asphalt	PCR 235 /F/A/W/T

FEET 0 1000 2000

METERS 0 500

Runway/taxway width, surface and strength			
RWY	147' 45M	Concrete and asphalt	PCR 783/F/C/W/T
TWY B	56' 17.0M	Asphalt	PCR 235 /F/A/W/T
TWY C	79' 24.0M	Asphalt	PCR 459 /F/B/W/U
TWY D	79' 24.0M	Asphalt	PCR 459 /F/B/W/U
TWY E	94' 28.5M	Asphalt	PCR 776 /F/D/W/T

NOTE
(See AD 2.13 for intersection take-off distances)

NOTE
1. Use of turning bay at rwy end for backtrack after landing mandatory for aircraft categories larger than B737-900.

RUNWAY CONFIGURATION		
Item	Length	Width
Strip	9842' 3000m (d - j)	984' 300m
THR 10 displaced	582' 177m (b - e)	
W end RESA	787' 240m (d - a)	295' 90m
E end RESA	787' 240m (j - l)	295' 90m
Rwy 10 CWY	459' 140m (i - k)	984' 300m
Rwy 28 CWY	492' 150m (e - c)	984' 300m

LEGEND	
Aerodrome reference point (ARP)	⊕
Building	▮
Ramp, taxiway, road	▬
Illuminated windsock	
Tower, antenna, etc. (lighted)	
Point Romeo	R
Lights	
Taxi holding position	

RWY	TORA	TODA	ASDA	LDA	START OF TORA/TODA/ASDA	POINT	ELEV	START OF LDA	POINT	ELEV	LIGHTING	BEARING
10	10029' 3057m (b - i)	10488' 3197m (b - k)	10029' 3057m (b - i)	9448' 2880m (e - i)	N12 07 52.42 W068 16 53.24	b	19' 5.9 m	N12 07 52.25 W068 16 47.38	e	18' 5.4m	SALS-Barette, threshold lights, high intensity rwy edge lights, PAPI R-3°	104°
28	9448' 2880m (i - e)	9940' 3030m (i - c)	9448' 2880m (i - e)	9448' 2880m (i - e)	N12 07 49.39 W068 15 12.18	i	20' 6.0 m	N12 07 49.39 W068 15 12.18	i	20' 6.0m	Threshold lights, high intensity rwy edge lights, PAPI L/R-3°	284°

CHANGES: Intersection take-off markings, wind sock symbol, PCR values and editorials.

AERO INFO DATE 18 DEC 2024