
AIRCRAFT PARKING/DOCKING CHART - ICAO
APRONS WEST A, B, C, D, E, F

AERODROME ELEV: 14' 4.2 m

JULIANA APPROACH: 128.950
JULIANA TOWER: 118.700

PRINCESS JULIANA INT (TNCM)
SINT MAARTEN

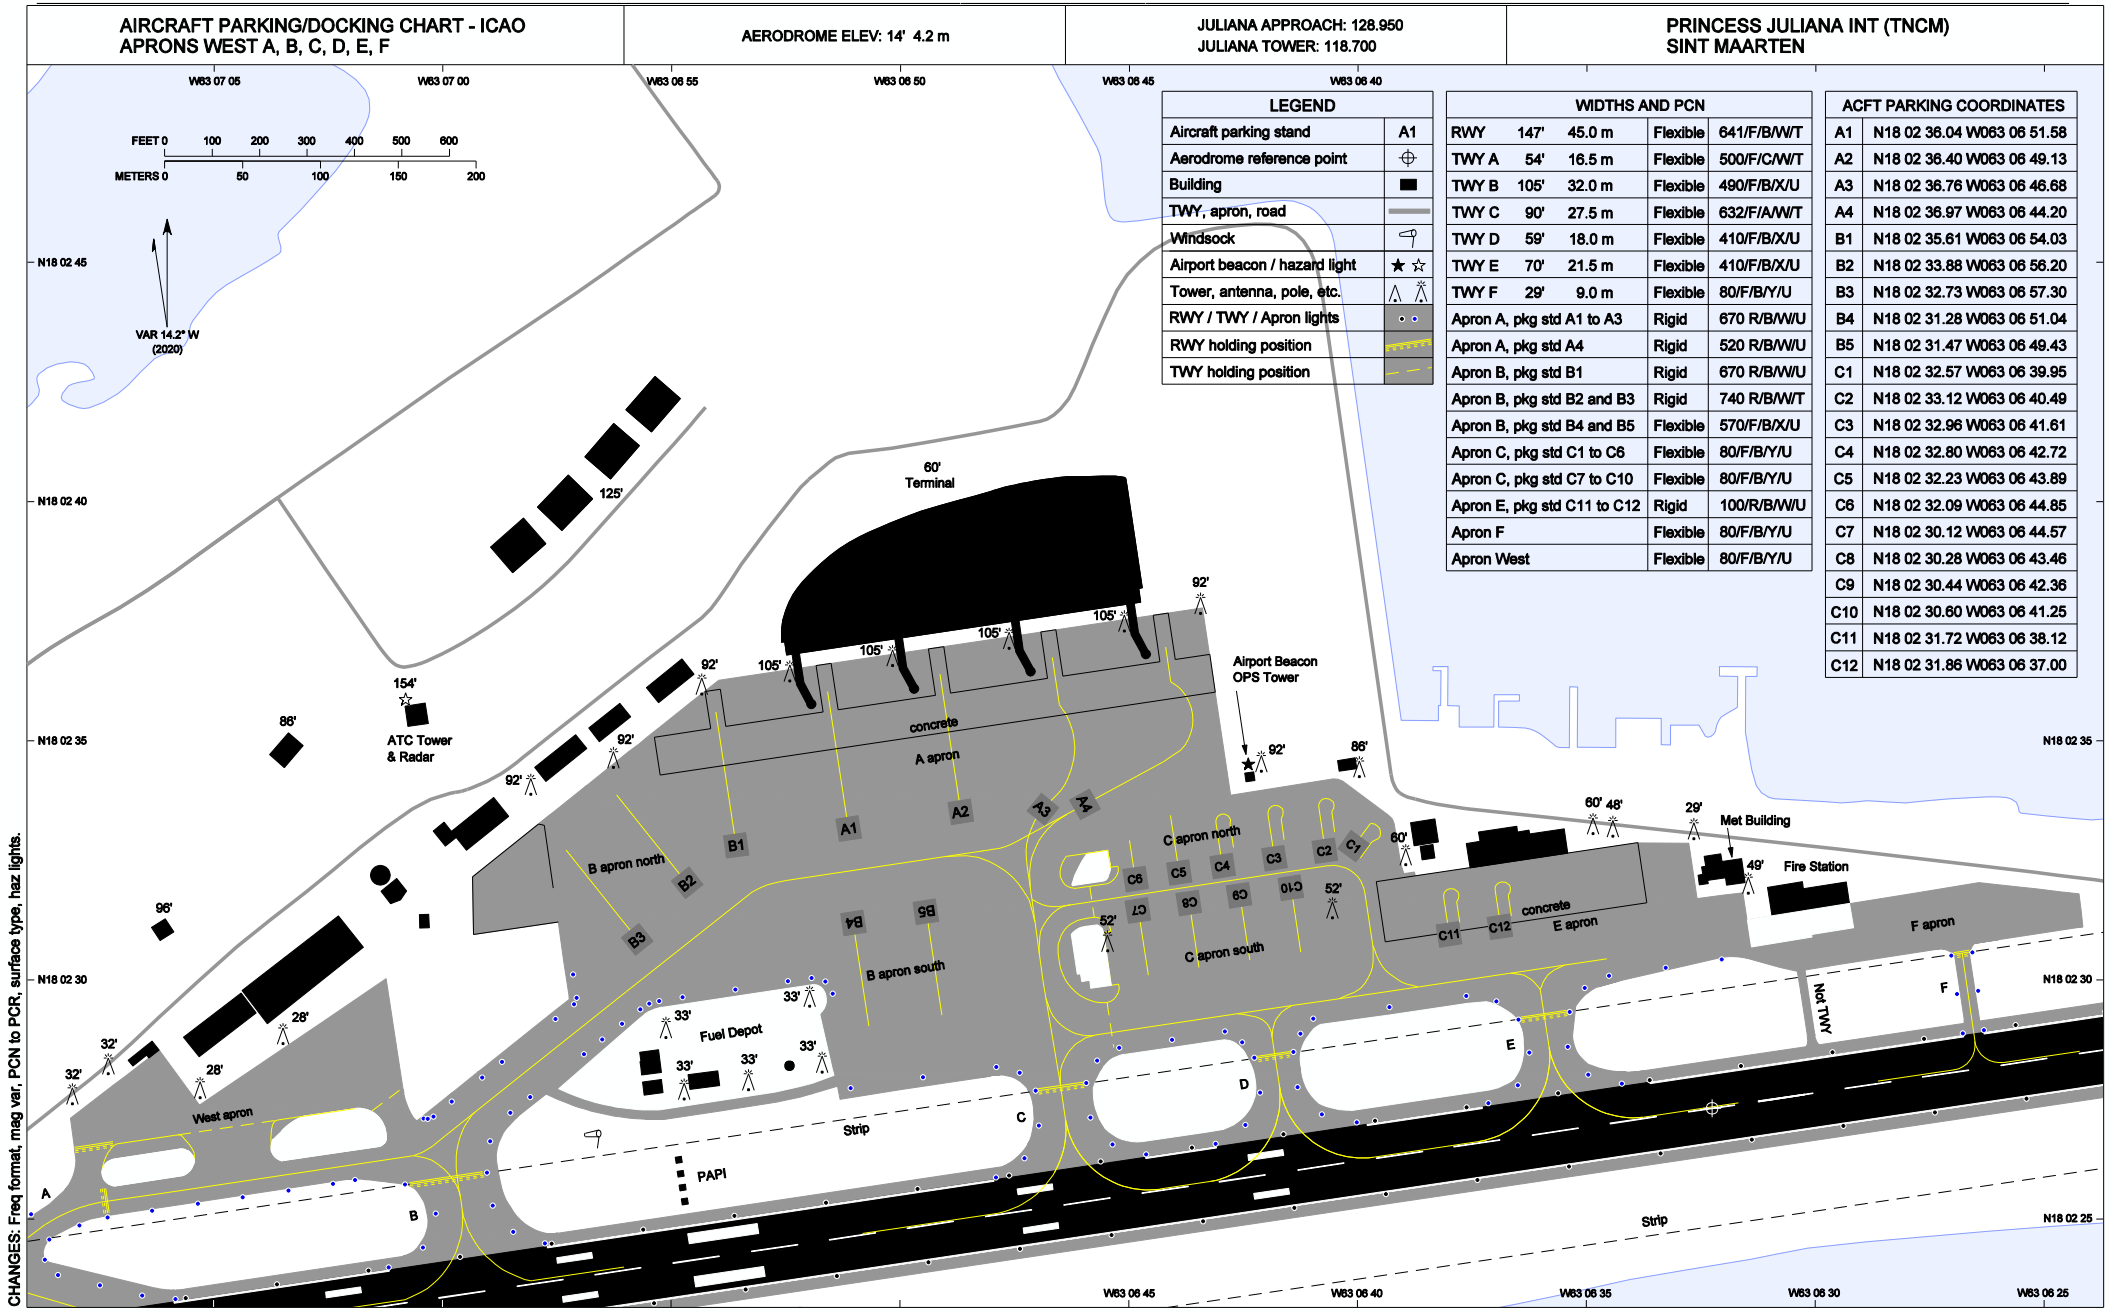

LEGEND	
Aircraft parking stand	A1
Aerodrome reference point	
Building	
TWY, apron, road	
Windsock	
Airport beacon / hazard light	
Tower, antenna, pole, etc.	
RWY / TWY / Apron lights	
RWY holding position	
TWY holding position	

WIDTHS AND PCN				
RWY	147'	45.0 m	Flexible	641/F/B/W/T
TWY A	54'	16.5 m	Flexible	500/F/C/W/T
TWY B	105'	32.0 m	Flexible	490/F/B/X/U
TWY C	90'	27.5 m	Flexible	632/F/A/W/T
TWY D	59'	18.0 m	Flexible	410/F/B/X/U
TWY E	70'	21.5 m	Flexible	410/F/B/X/U
TWY F	29'	9.0 m	Flexible	80/F/B/Y/U
Apron A, pkg std A1 to A3			Rigid	670 R/B/W/U
Apron A, pkg std A4			Rigid	520 R/B/W/U
Apron B, pkg std B1			Rigid	670 R/B/W/U
Apron B, pkg std B2 and B3			Rigid	740 R/B/W/T
Apron B, pkg std B4 and B5			Flexible	570/F/B/X/U
Apron C, pkg std C1 to C6			Flexible	80/F/B/Y/U
Apron C, pkg std C7 to C10			Flexible	80/F/B/Y/U
Apron E, pkg std C11 to C12			Rigid	100/R/B/W/U
Apron F			Flexible	80/F/B/Y/U
Apron West			Flexible	80/F/B/Y/U

ACFT PARKING COORDINATES	
A1	N18 02 36.04 W063 06 51.58
A2	N18 02 36.40 W063 06 49.13
A3	N18 02 36.76 W063 06 46.68
A4	N18 02 36.97 W063 06 44.20
B1	N18 02 35.61 W063 06 54.03
B2	N18 02 33.88 W063 06 56.20
B3	N18 02 32.73 W063 06 57.30
B4	N18 02 31.28 W063 06 51.04
B5	N18 02 31.47 W063 06 49.43
C1	N18 02 32.57 W063 06 39.95
C2	N18 02 33.12 W063 06 40.49
C3	N18 02 32.96 W063 06 41.61
C4	N18 02 32.80 W063 06 42.72
C5	N18 02 32.23 W063 06 43.89
C6	N18 02 32.09 W063 06 44.85
C7	N18 02 30.12 W063 06 44.57
C8	N18 02 30.28 W063 06 43.46
C9	N18 02 30.44 W063 06 42.36
C10	N18 02 30.60 W063 06 41.25
C11	N18 02 31.72 W063 06 38.12
C12	N18 02 31.86 W063 06 37.00

CHANGES: Freq format, mag var, PCN to PCR, surface type, haz lights.