
AIRCRAFT PARKING/DOCKING CHART - ICAO
APRONS G, H

APRON G ELEV	4'	1.2 M
APRON H ELEV	5'	1.4 M

JULIANA TOWER: 118.700

PRINCESS JULIANA INT (TNCM)
SINT MAARTEN

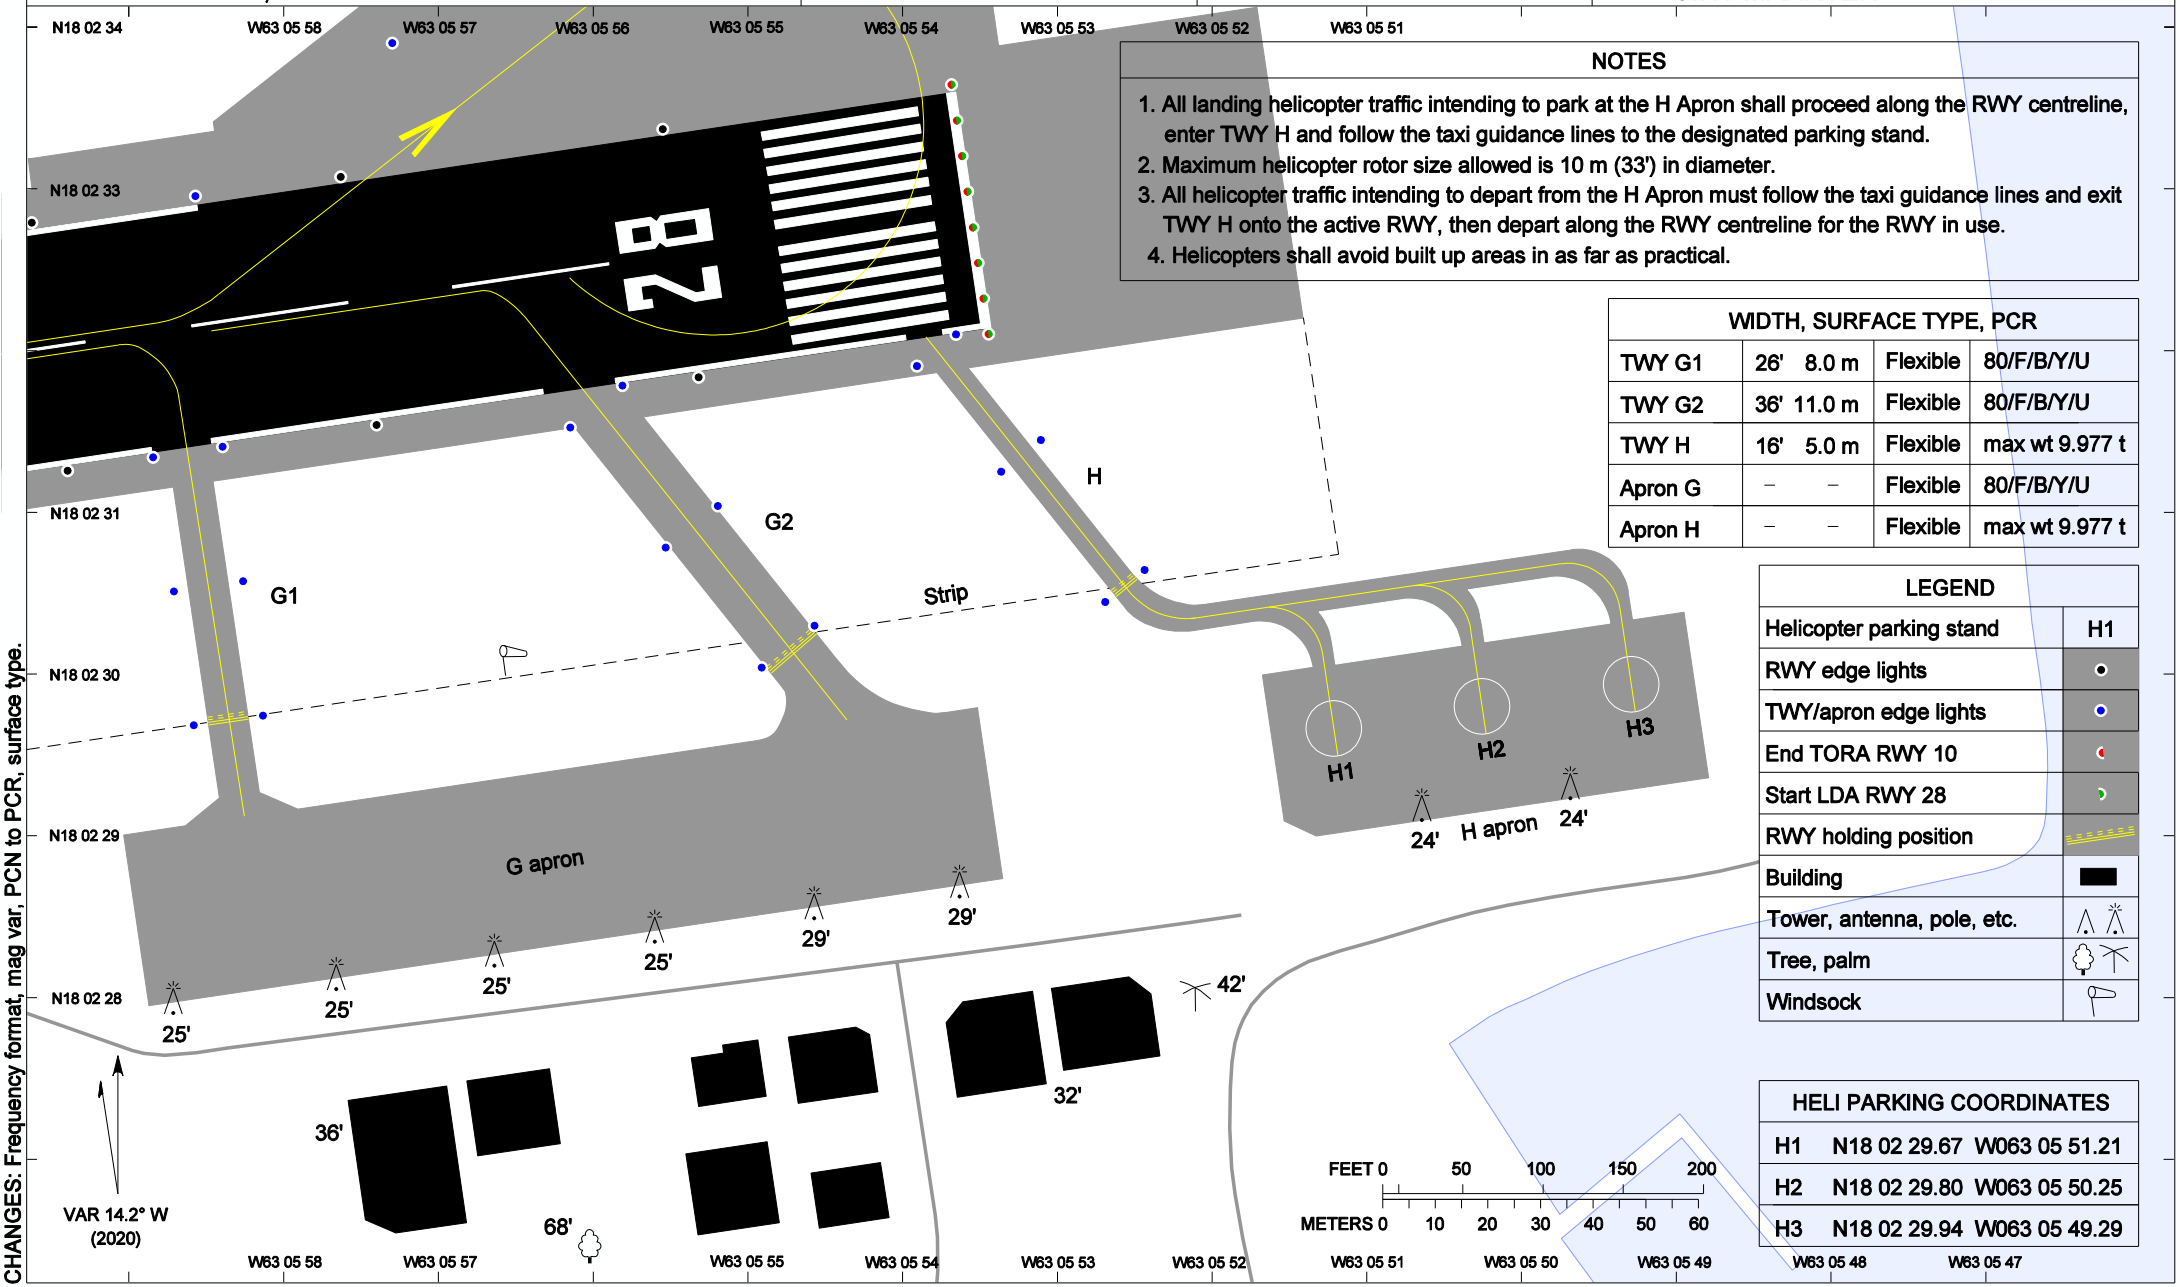

NOTES

1. All landing helicopter traffic intending to park at the H Apron shall proceed along the RWY centreline, enter TWY H and follow the taxi guidance lines to the designated parking stand.
2. Maximum helicopter rotor size allowed is 10 m (33') in diameter.
3. All helicopter traffic intending to depart from the H Apron must follow the taxi guidance lines and exit TWY H onto the active RWY, then depart along the RWY centreline for the RWY in use.
4. Helicopters shall avoid built up areas in as far as practical.

WIDTH, SURFACE TYPE, PCR				
TWY G1	26'	8.0 m	Flexible	80/F/B/Y/U
TWY G2	36'	11.0 m	Flexible	80/F/B/Y/U
TWY H	16'	5.0 m	Flexible	max wt 9.977 t
Apron G	–	–	Flexible	80/F/B/Y/U
Apron H	–	–	Flexible	max wt 9.977 t

LEGEND	
Helicopter parking stand	H1
RWY edge lights	
TWY/apron edge lights	
End TORA RWY 10	
Start LDA RWY 28	
RWY holding position	
Building	
Tower, antenna, pole, etc.	
Tree, palm	
Windsock	

HELI PARKING COORDINATES	
H1	N18 02 29.67 W063 05 51.21
H2	N18 02 29.80 W063 05 50.25
H3	N18 02 29.94 W063 05 49.29

CHANGES: Frequency format, mag var, PCN to PCR, surface type.

AERO INFO DATE 17 APR 2025