
AERODROME CHART - ICAO	ARP: N 18 12 17.28 W 063 03 13.88	AERODROME ELEV 127'	WALLBLAKE TOWER 118.5 JULIANA APPROACH 128.95 (PRIMARY), 118.7	DIMENSIONS IN FEET *(METERS)* ELEVATIONS IN FEET BEARINGS ARE MAGNETIC	WALLBLAKE (TQPF) THE VALLEY, ANGUILLA

W63 03 40 W63 03 30 W63 03 20 W63 03 10 W63 03 00 W63 02 50

N18 12 30 N18 12 20 N18 12 10

PARKING SPOT COORDINATES	
1	N18 12 21.99 W063 03 11.50
2	N18 12 22.00 W063 03 10.67
3	N18 12 22.00 W063 03 09.86
4	N18 12 20.75 W063 03 10.33
5	N18 12 20.75 W063 03 08.90
6	N18 12 21.98 W063 03 08.24
7	N18 12 21.99 W063 03 07.43
8	N18 12 21.99 W063 03 06.61
9	N18 12 20.74 W063 03 07.36

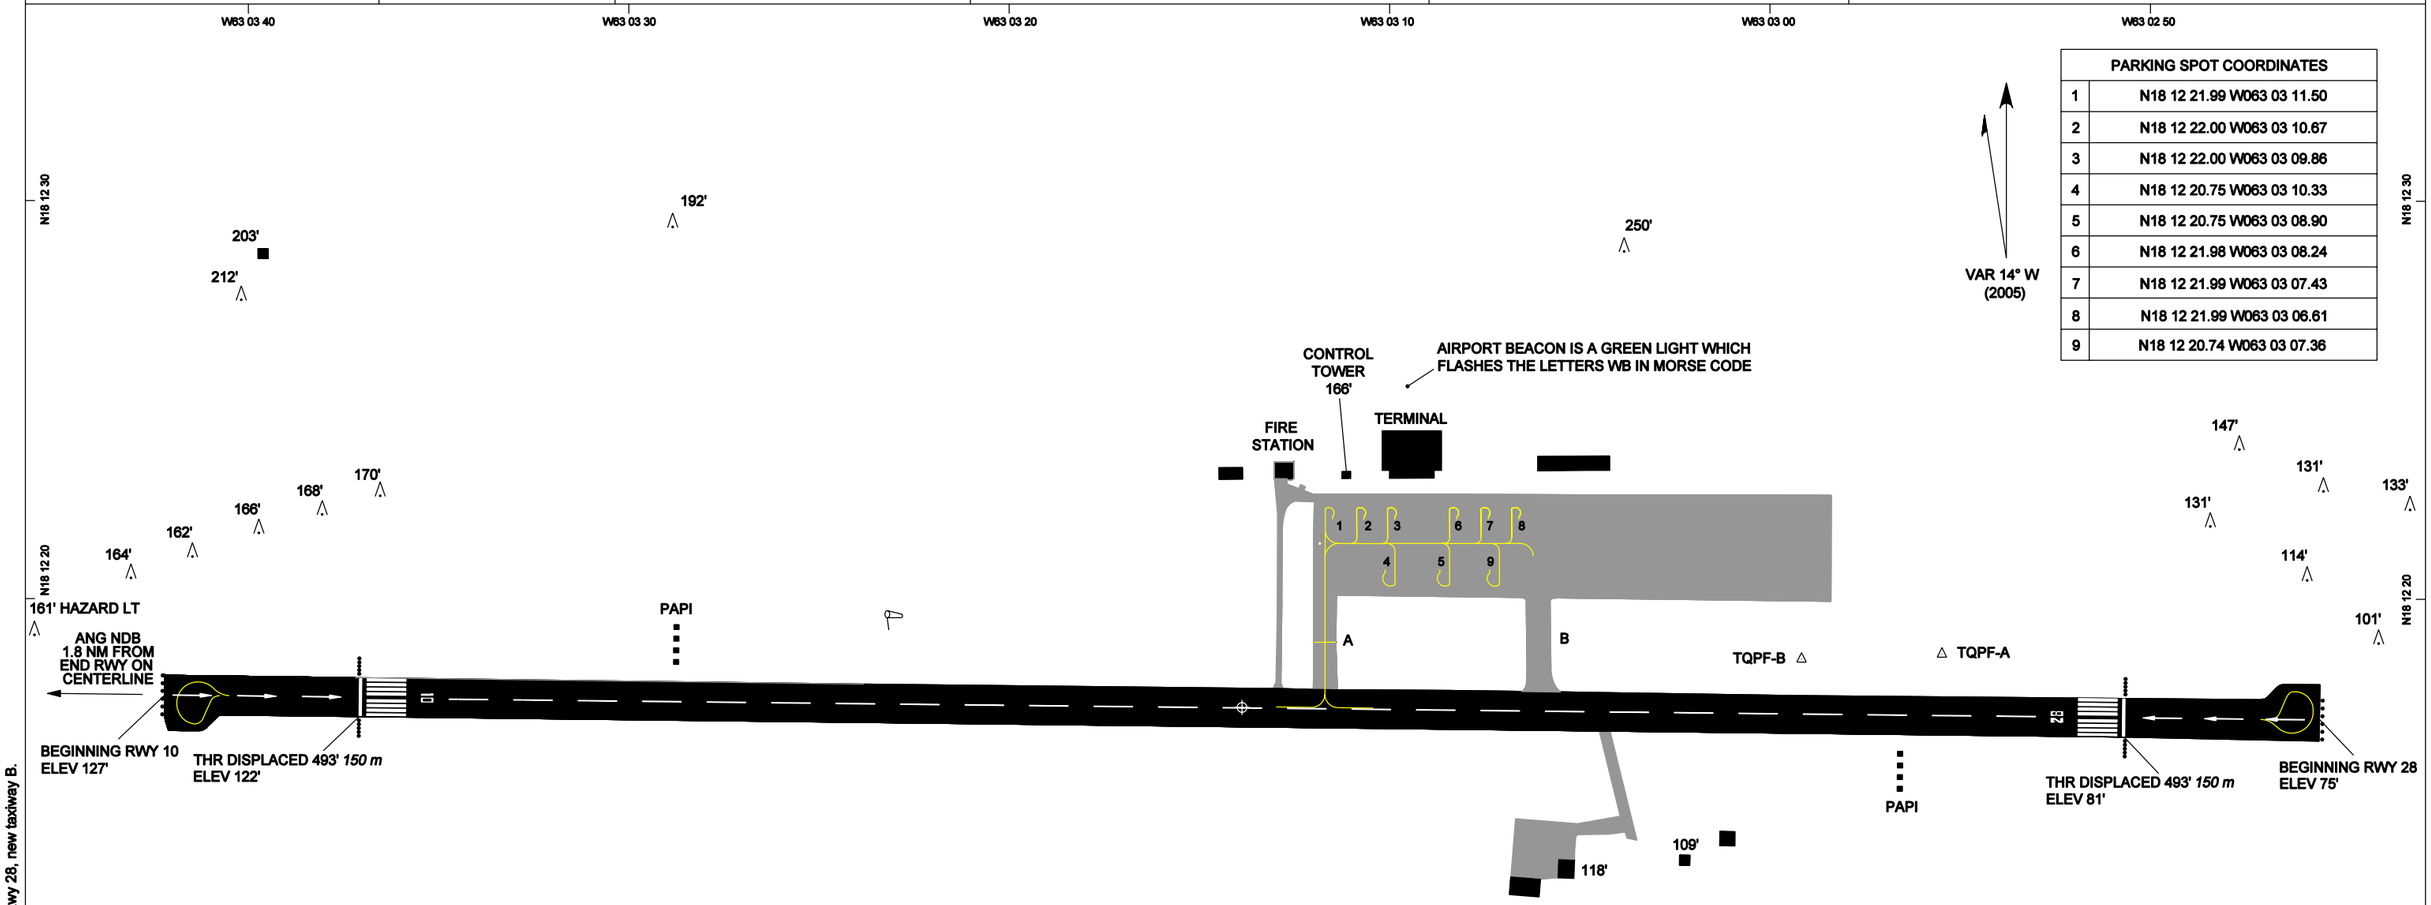

LEGEND	
AERODROME REFERENCE POINT (ARP)	⊕
SURVEY STATION	△
BUILDING	■
ROAD, RAMP, TAXIWAY	▬
WINDSOCK	⚑
TREE	✳
POLE, TOWER, SPIRE, ANTENNA, ETC.	⍋
LIGHTS	• • • • •

RESTRICTIONS
- CONTROLLED AIRSPACE.
- VISIBILITY EXEMPTED BY DAY.
- INSTRUMENT RESTRICTED BY NIGHT.

CAUTION
- NUMEROUS POLES AND ANTENNAS IN VICINITY OF AERODROME.

FEET 0 1000 2000

METERS 0 500

W63 03 40 W63 03 30 W63 03 20 W63 03 10 W63 03 00 W63 02 50

RWY	LIGHTING / RWY SURFACE	LANDING BEYOND THRESHOLD	GLIDE SLOPE	TAKE - OFF RUN AVAILABLE	WIDTH	END RUNWAY	DISPLACED THRESHOLD	DIRECTION	BEARING STRENGTH
10	RL, PAPI-L (3°) / ASPHALT	4968' *1515 m*		5461' *1665 m*	98'	N18 12 17.58 W063 03 42.20	N18 12 17.53 W063 03 37.08	105°	RWY/TWY/RAMP: PCN 22 F/A/W/T
28	RL, PAPI-L (3°) / ASPHALT	4968' *1515 m*		5461' *1665 m*	*30 m*	N18 12 16.97 W063 02 45.56	N18 12 17.03 W063 02 50.67	285°	

CHANGES: runway and ramp extended, Rwy 28 threshold displaced, PAPI added Rwy 28, new taxiway B.